ΑΠΟΣΠΑΣΜΑ MAPS.GOV.GR

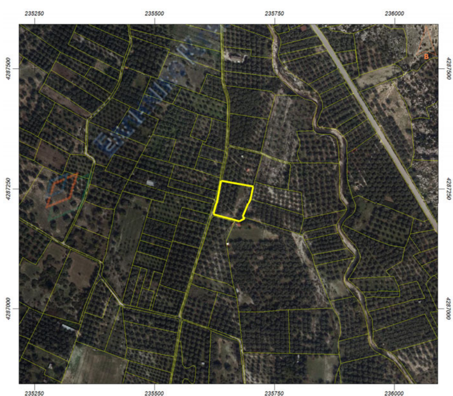

ΑΠΟΣΠΑΣΜΑ ΚΥΡΩΜΕΝΟΥ ΔΑΣΙΚΟΥ ΧΑΡΤΗ

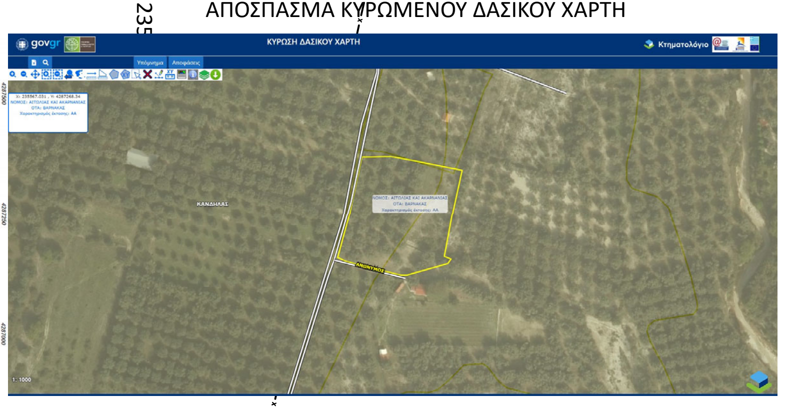

ΠΙΝΑΚΑΣ ΣΥΝΤΕΤΑΓΜΕΝΩΝ ΚΟΡΥΦΩΝ ΤΟΡΟPROP ΕΓΣΑ'87

α/α	X	Y	Απόσταση (μ.)
Α1	235638.96	4287266.59	Α1-Α2=3.52
Α2	235638.20	4287263.15	Α2-Α3=27.17
Α3	235632.47	4287236.59	Α3-Α4=13.27
Α4	235629.77	4287223.61	Α4-Α5=3.40
Α5	235628.82	4287220.34	Α5-Α6=13.20
Α6	235625.34	4287207.60	Α6-Α7=8.87
Α7	235623.03	4287199.04	Α7-Α8=2.41
Α8	235622.37	4287196.72	Α8-Α9=2.49
Α9	235624.62	4287195.67	Α9-Α10=2.08
Α10	235626.50	4287194.78	Α10-Α11=1.79
Α11	235628.13	4287194.03	Α11-Α12=6.16
Α12	235634.11	4287192.52	Α12-Α13=10.37
Α13	235644.18	4287190.04	Α13-Α14=20.64
Α14	235664.20	4287185.03	Α14-Α15=15.47
Α15	235679.48	4287182.59	Α15-Α16=18.11
Α16	235694.11	4287193.27	Α16-Α17=3.97
Α17	235697.31	4287195.61	Α17-Α18=4.92
Α18	235692.76	4287197.47	Α18-Α19=3.42
Α19	235693.38	4287200.83	Α19-Α20=25.25
Α20	235698.03	4287225.65	Α20-Α21=29.28
Α21	235704.31	4287254.25	Α21-Α22=2.99
Α22	235701.39	4287254.90	Α22-Α23=8.03
Α23	235693.52	4287256.44	Α23-Α24=9.90
Α24	235683.81	4287258.39	Α24-Α25=5.56
Α25	235678.36	4287259.49	Α25-Α26=6.42
Α26	235672.06	4287260.70	Α26-Α27=9.99
Α27	235662.24	4287262.55	Α27-Α28=5.01
Α28	235657.30	4287263.41	Α28-Α1=18.62

Εμβαδόν (Α1,Α2,...,Α28,Α1)=4973.31 τ.μ.

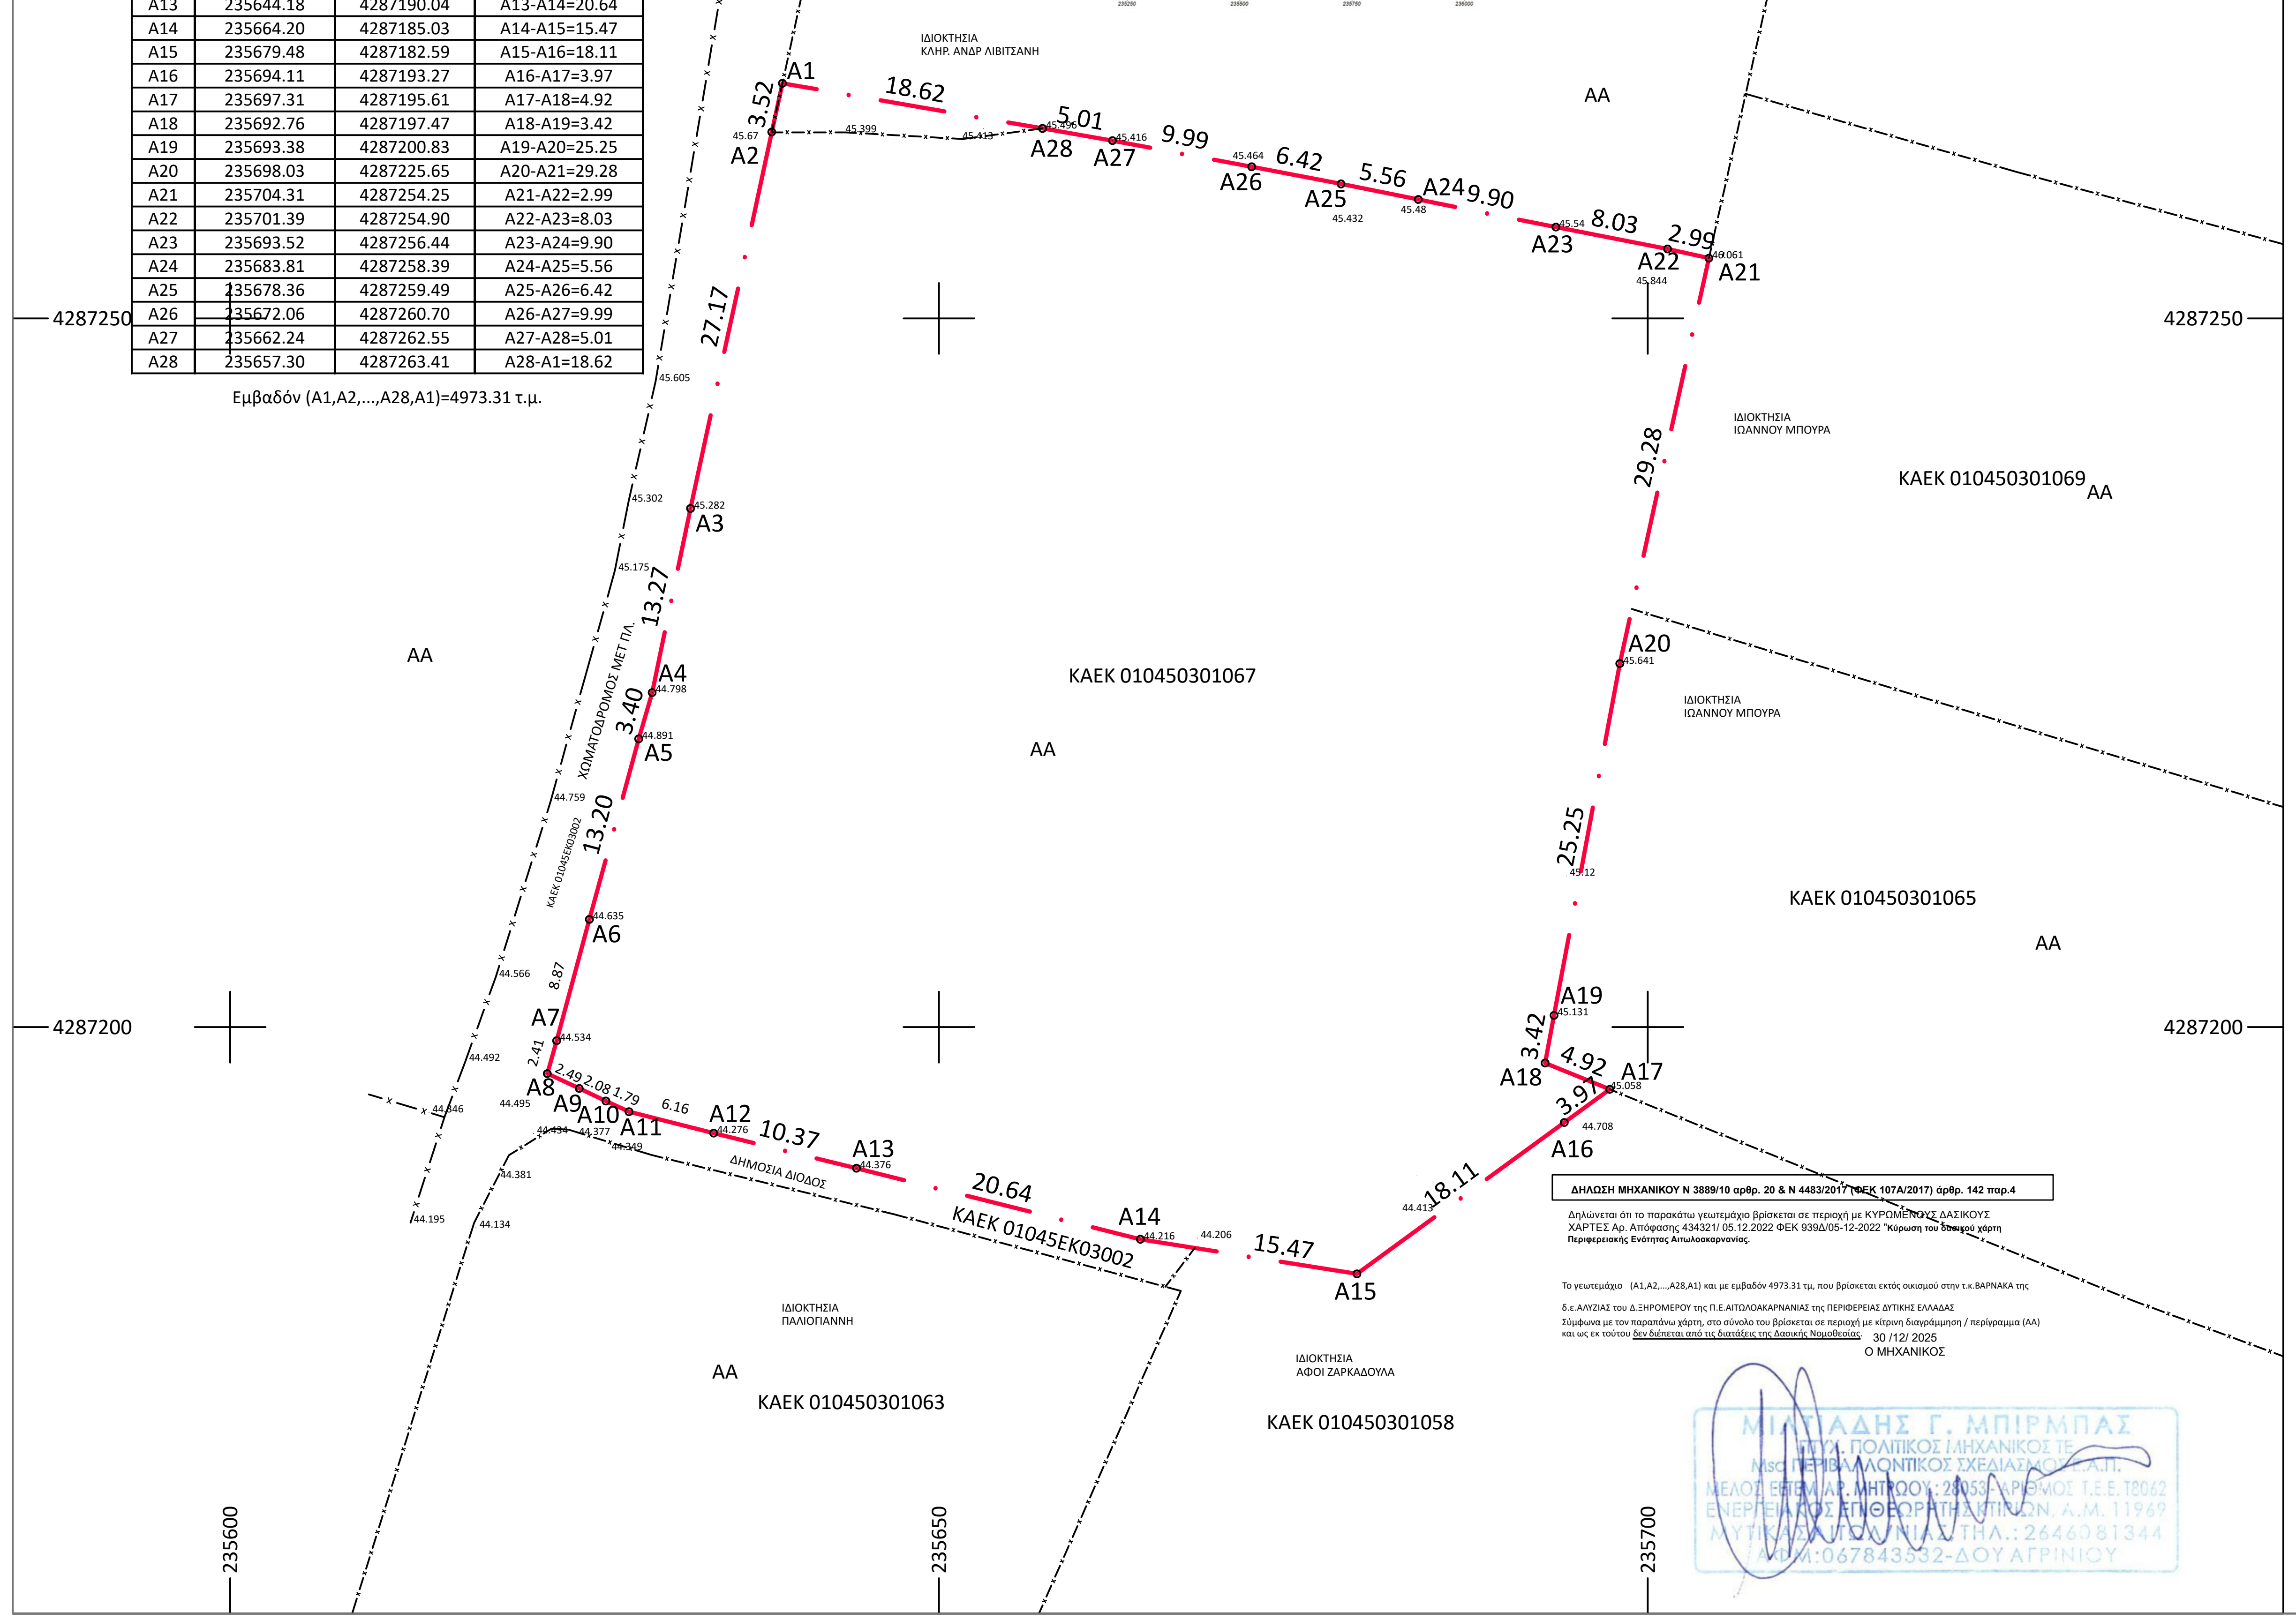

ΔΗΛΩΣΗ ΜΗΧΑΝΙΚΟΥ Ν 3889/10 αρθρ. 20 & Ν 4483/2017 (ΦΕΚ 107Α/2017) άρθρ. 142 παρ.4

Δηλώνεται ότι το παρακάτω γεωτεμάχιο βρίσκεται σε περιοχή με ΚΥΡΩΜΕΝΟΥΣ ΔΑΣΙΚΟΥΣ ΧΑΡΤΕΣ Αρ. Απόφασης 434321/ 05.12.2022 ΦΕΚ 939Δ/05-12-2022 **"Κύρωση του δασικού χάρτη Περιφερειακής Ενότητας Αιτωλοακαρνανίας.**

Το γεωτεμάχιο (Α1,Α2,...,Α28,Α1) και με εμβαδόν 4973.31 τμ, που βρίσκεται εκτός οικισμού στην τ.κ.ΒΑΡΝΑΚΑ της

δ.ε.ΑΛΥΖΙΑΣ του Δ.ΞΗΡΟΜΕΡΟΥ της Π.Ε.ΑΙΤΩΛΟΑΚΑΡΝΑΝΙΑΣ της ΠΕΡΙΦΕΡΕΙΑΣ ΔΥΤΙΚΗΣ ΕΛΛΑΔΑΣ

Σύμφωνα με τον παραπάνω χάρτη, στο σύνολο του βρίσκεται σε περιοχή με κίτρινη διαγράμμηση / περίγραμμα (ΑΑ) και ως εκ τούτου δεν διέπεται από τις διατάξεις της Δασικής Νομοθεσίας.

30 /12/ 2025
Ο ΜΗΧΑΝΙΚΟΣ

ΜΙΛΤΙΑΔΗΣ Γ. ΜΠΙΡΜΠΑΣ
ΠΤΥΧ. ΠΟΛΙΤΙΚΟΣ ΜΗΧΑΝΙΚΟΣ ΤΕ
Msc ΠΕΡΙΒΑΛΛΟΝΤΙΚΟΣ ΣΧΕΔΙΑΣΜΟΣ Ε.Α.Π.
ΜΕΛΟΣ ΕΕΤΕΜ ΑΡ. ΜΗΤΡΩΟΥ: 28053 - ΑΡΙΘΜΟΣ Τ.Ε.Ε. 78062
ΕΝΕΡΓΕΙΑΚΟΣ ΕΠΙΘΕΩΡΗΤΗΣ ΚΤΙΡΙΩΝ, Α.Μ. 11969
ΜΥΤΙΚΑΣ ΑΙΤΩΛ/ΝΙΑΣ ΤΗΛ.: 2646081344
ΑΦΜ:067843532-ΔΟΥ ΑΓΡΙΝΙΟΥ

ΟΡΟΙ ΔΟΜΗΣΗΣ ΕΚΤΟΣ ΣΧΕΔΙΟΥ ΦΕΚ 245Α 9-12-2020

Άρθρο 32
Εκτός σχεδίου δόμηση

1. Τα γήπεδα που βρίσκονται εκτός σχεδίων πόλεως, εκτός ορίων των νομίμως υφισταμένων οικισμών προ του έτους 1923, που στερούνται ρυμοτομικού σχεδίου, και εκτός περιοχών, στις οποίες έχουν καθορισθεί χρήσεις γης, όροι και περιορισμοί δόμησης από εργαλεία πολεοδομικού σχεδιασμού πρώτου επιπέδου ή από διατάγματα που καθορίζουν όρους και περιορισμούς δόμησης σε περιοχές εκτός σχεδίου, όπως τα διατάγματα της παρ. 2 του άρθρου 10 του από 17.7/ 16.8.1923 (Α΄ 228) ν.δ. ή Ζώνες Οικιστικού Ελέγχου του άρθρου 29 του ν. 1337/1983 (Α΄ 33) ή Ε.Σ.Χ.Α.Δ.Α. του άρθρου 12 του ν. 3986/2011 (Α΄ 152) ή Ε.Σ.Χ.Α.Σ.Ε. του άρθρου 24 του ν. 3894/2010 (Α΄ 204), διέπονται από τις διατάξεις του παρόντος Κεφαλαίου, καθώς και από την κείμενη νομοθεσία, ιδίως δε από τις διατάξεις του από 6.10.1978 π.δ. (Δ΄ 538) και του από 24.5.1985 π.δ. (Δ΄ 270), που δεν έρχονται σε αντίθεση με τις διατάξεις του παρόντος. Στα γήπεδα αυτά, οι οικοδομικές άδειες επιβαρύνονται με τέλος πέντε τοις εκατό (5%) επί του κόστους της οικοδομικής άδειας, το οποίο αποδίδεται στο Πράσινο Ταμείο, για τη χρηματοδότηση δράσεων στις εκτός σχεδίου περιοχές που αντισταθμίζουν την επιβάρυνση του περιβάλλοντος από το γεγονός ότι δομούνται περιοχές που κατ' αρχήν δεν προορίζονται για δόμηση.

ΑΡΘΡΟ 33

Για τις ανάγκες της δόμησης των κτιρίων της παρ. 1 του άρθρου 32, ο μέγιστος συντελεστής δόμησης ανέρχεται καταρχήν σε 0,18, το μέγιστο ποσοστό κάλυψης σε δέκα τοις εκατό (10%) και ο μέγιστος αριθμός ορόφων σε δύο (2).

2. Το ανώτατο ύψος των κτισμάτων απαγορεύεται να υπερβαίνει τον υδροκρίτη.

3. Στις πιο κάτω περιπτώσεις, ισχύουν ειδικά οι εξής όροι δόμησης:

α) αα) Σε γεωργοκτηνοτροφικά, γεωργοπτηνοτροφικά κτίρια, κτίρια υδατοκαλλιεργειών, στέγαστρα σφαγής, γεωργικές αποθήκες, δεξαμενές, θερμοκήπια και λοιπές γεωργικές κατασκευές του άρθρου 2 του από 24.5.1985 προεδρικού διατάγματος (Δ΄ 270), η παρέκκλιση του συντελεστή δόμησης που προβλέπεται στην περ. ε΄ της παρ. 1 του ίδιου άρθρου δεν μπορεί να υπερβεί το 0,8.
αβ) Οι δεξαμενές καλλιέργειας υδρόβιων οργανισμών εντάσσονται στις παρεκκλίσεις της περ. α΄ της παρ. 2 του από 24.5.1985 προεδρικού διατάγματος (Δ΄ 270) αλλά το μέγιστο ύψος αυτών ορίζεται σε 50 εκατοστά.
β) Σε βιομηχανικές εγκαταστάσεις του άρθρου 4 του από 24.5.1985 προεδρικού διατάγματος (Δ΄ 270) ο μέγιστος συντελεστής δόμησης δεν μπορεί να υπερβεί το 0,6 και ο μέγιστος συντελεστής κατ' όγκον εκμετάλλευσης το 4.
γ) Σε κτίρια που προορίζονται για αμιγή χρήση γραφείων ή καταστημάτων του άρθρου 5 του από 24.5.1985 π.δ. η μέγιστη επιφάνεια του κτιρίου, καθώς και η συνολική επιφάνεια των ορόφων δεν μπορούν να υπερβαίνουν τα πεντακόσια πενήντα (550) τ.μ.. Η παρέκκλιση του συντελεστή δόμησης, που προβλέπεται στην παρ. 2 του ίδιου άρθρου, χορηγείται με απόφαση του Υπουργού Περιβάλλοντος και Ενέργειας ύστερα από γνωμοδότηση του Κεντρικού Συμβουλίου Πολεοδομικών Θεμάτων και Αμφισβητήσεων (ΚΕ.ΣΥ.ΠΟ.ΘΑ.) ή του Συμβουλίου Μητροπολιτικού Σχεδιασμού, κατά περίπτωση και δεν μπορεί να υπερβεί το 0,18 και η παρέκκλιση του ποσοστού κάλυψης δεν μπορεί να υπερβεί το δέκα οκτώ τοιςεκατό (18%).
δ) Σε κτίρια κατοικίας της περ. ΙΙ.1 του άρθρου 1 του προεδρικού διατάγματος 59/2018 (Α΄ 114), η μέγιστη επιτρεπομένη επιφάνεια του κτιρίου ως και η συνολική επιφάνεια των ορόφων δεν επιτρέπεται να υπερβαίνει:
δα) Για γήπεδα εμβαδού μεγαλύτερου των τεσσάρων χιλιάδων (4.000) τ.μ. μέχρι και οχτώ χιλιάδες (8.000) τ.μ., για μεν τα πρώτα τέσσερις χιλιάδες (4.000) τ.μ. τα εκατόν
11692 ΕΦΗΜΕΡΙΔΑ ΤΗΣ ΚΥΒΕΡΝΗΣΕΩΣ Τεύχος Α' 245/09.12.2020
ογδόντα έξι (186) τ.μ., για δε τα λοιπά το γινόμενο του υπολοίπου εμβαδού του γηπέδου επί τον συντελεστή δόμησης 0,018.
δβ) Για γήπεδα εμβαδού μεγαλύτερου των οχτώ χιλιάδων (8.000) τ.μ., για μεν τα πρώτα οχτώ χιλιάδες (8.000)τ.μ. τα διακόσια πενήντα οχτώ (258) τ.μ., για δε τα λοιπά το γινόμενο του υπολοίπου εμβαδού του γηπέδου επί τον συντελεστή δόμησης 0,009 μη δυναμένη σε καμία περίπτωση να υπερβεί τα τριακόσια εξήντα (360) τ.μ..
δγ) Για γήπεδα με εμβαδόν πολλαπλάσιο του κατά κανόνα αρτίου (4.000 τ.μ.), για τα οποία συντρέχουν οι προϋποθέσεις κατάτμησης, η μέγιστη επιφάνεια κτιρίου ισούται με το άθροισμα του εμβαδού των κτιρίων που θα επιτρεπόταν να ανεγερθούν σε κάθε γήπεδο μετά την κατάτμηση, μειωμένη κατά δέκα πέντε τοις εκατό (15%), και υπό τις προϋποθέσεις ότι: α) θα ανεγερθεί μια οικοδομή και β) το γήπεδο θα παραμείνει ενιαίο. Μεταβιβάσεις κατά παράβαση των προϋποθέσεων αυτών είναι αυτοδικαίως άκυρες.
ε) Σε κτίρια που προορίζονται για εμπορικές αποθήκες του άρθρου 9 του από 24.5.1985 προεδρικού διατάγματος, ο μέγιστος συντελεστής δόμησης ορίζεται σε 0,18 και το μέγιστο ποσοστό κάλυψης σε δέκα οχτώ τοις εκατό (18%). Η παρέκκλιση του συντελεστή δόμησης που προβλέπεται στις περ. ε΄, στ΄ και ζ΄ της παρ. 2 του ίδιου άρθρου, χορηγείται με απόφαση του Υπουργού Περιβάλλοντος και Ενέργειας ύστερα από γνωμοδότηση του Κεντρικού Συμβουλίου Πολεοδομικών Θεμάτων και Αμφισβητήσεων (ΚΕ.ΣΥ.ΠΟ.ΘΑ.) ή του Συμβουλίου Μητροπολιτικού Σχεδιασμού, κατά περίπτωση.

4. Εάν εμβαδόν γηπέδου που υπερέβαινε τα 4.000 τ.μ. απομειώθηκε λόγω απαλλοτρίωσης, διάνοιξης διεθνούς, εθνικής, επαρχιακής ή δημοτικής οδού ή αναδασμού, το γήπεδο θεωρείται άρτιο, εάν το εμβαδόν του υπερβαίνει τα 2.000 τ.μ. και έχει πρόσωπο σε διεθνή, εθνική, επαρχιακή ή δημοτική οδό τουλάχιστον είκοσι πέντε (25) μ..

5. Στις εκτός σχεδίου περιοχές επιτρέπεται η συνένωση όμορων γηπέδων, υπό τις εξής προϋποθέσεις:
α) το νέο γήπεδο που προκύπτει μετά τη συνένωση έχει εμβαδόν τουλάχιστον 4.000 τ.μ. και,
β) τουλάχιστον ένα από τα γήπεδα που συνενώνονται είναι άρτιο και οικοδομήσιμο με τις διατάξεις που ίσχυαν μέχρι την έναρξη ισχύος του παρόντος νόμου

ΟΡΟΙ ΔΟΜΗΣΗΣ ΕΚΤΟΣ ΣΧΕΔΙΟΥ ΦΕΚ 245Α 9-12-2020 ΑΡΤΙΟΤΗΤΑ

Άρθρο 40
Μεταβατικές - εξουσιοδοτικές διατάξεις

1. Εάν, μέχρι την έγκριση Τοπικού Πολεοδομικού Σχεδίου ή Ειδικού Πολεοδομικού Σχεδίου και πάντως για χρονικό διάστημα που δεν υπερβαίνει τα δύο (2) έτη από την έναρξη ισχύος του παρόντος χορηγηθεί προέγκριση οικονομικής άδειας, μπορούν να οικοδομούνται ακίνητα, τα οποία:
α) κατά την έναρξη ισχύος του παρόντος έχουν πρόσωπο σε διεθνείς, εθνικές, επαρχιακές, δημοτικές και κοινοτικές οδούς, καθώς και σε εγκαταλελειμμένα τμήματα αυτών και σε σιδηροδρομικές γραμμές και εφόσον έχουν: αα) Τα γήπεδα που υφίστανται κατά την 12η.11.1962, ημέρα δημοσίευσης του από 24.10.1962 βασιλικού διατάγματος (Δ΄ 142), ελάχιστο πρόσωπο: δέκα (10) μέτρα, ελάχιστο βάθος: δεκαπέντε (15) μέτρα, ελάχιστο εμβαδόν: επτακόσια πενήντα 750 τ.μ.,
αβ) υφίστανται κατά την 12η.9.1964, ημέρα έναρξης ισχύος του από 21.7.1964 βασιλικού διατάγματος (Δ΄ 141), ελάχιστο πρόσωπο: είκοσι (20) μέτρα, ελάχιστο βάθος: τριάντα πέντε (35) μέτρα, ελάχιστο εμβαδόν 1.200 τ.μ.,
β) έχουν πρόσωπο σε εθνική, επαρχιακή, ή δημοτική οδό εφόσον υφίστανται κατά την 17η.10.1978, ημέρα έναρξης ισχύος του από 6.10.1978 προεδρικού διατάγματος (Δ΄ 538), και έχουν ελάχιστο πρόσωπο: είκοσι πέντε (25) μ., ελάχιστο βάθος: σαράντα (40) μ. και ελάχιστο εμβαδόν δύο χιλιάδες (2.000) τ.μ.,
γ) έχουν πρόσωπο σε εθνική, επαρχιακή, ή δημοτική οδό, εφόσον υφίστανται κατά την 17η.10.1978, και έχουν ελάχιστο πρόσωπο: είκοσι πέντε (25) μ., ελάχιστο βάθος: σαράντα (40) μ. και ελάχιστο εμβαδόν δύο χιλιάδες (2.1) τ.μ.,
δ) βρίσκονται εντός της ζώνης των πόλεων, κωμών και οικισμών και είχαν κατά την 24η.4.1977, ημέρα έναρξης ισχύος του από 5.4.1977 προεδρικού διατάγματος (Δ΄ 133), και ελάχιστο εμβαδόν: δύο χιλιάδες (2.000) τ.μ.,
ε) είναι άρτια και οικοδομήσιμα και απομειούνται συνεπεία απαλλοτριώσεων ή διάνοιξης διεθνών, εθνικών ή επαρχιακών οδών, εφόσον μετά από την απομείωση αυτή έχουν τα όρια αρτιότητας και τις λοιπές προϋποθέσεις των γηπέδων της περ. δ΄,
στ) σε περιπτώσεις αναδασμών, γήπεδα που δημιουργούνται και δίνονται σε δικαιούχους σε ανταλλαγή
Τεύχος Α' 245/09.12.2020 ΕΦΗΜΕΡΙΔΑ ΤΗΣ ΚΥΒΕΡΝΗΣΕΩΣ 11699
αρτίων και οικοδομήσιμων γηπέδων, εφόσον μετά από τον αναδασμό αυτόν έχουν τα όρια αρτιότητας και τις προϋποθέσεις των γηπέδων της περ. δ΄,
ζ) έχουν ελάχιστο εμβαδόν 4.000 τ.μ., όταν επ' αυτών ανεγείρονται τουριστικές εγκαταστάσεις και
η) δημιουργήθηκαν από την 17η.10.1978 μέχρι την 31η.12.2003, ημέρα έναρξης ισχύος του ν. 3212/2003 (Α΄ 308), με ελάχιστο εμβαδόν 4000 τ.μ..

ΔΗΛΩΣΗ ΜΗΧΑΝΙΚΟΥ (Ν. 651/77)

Δηλώνω σύμφωνα με το νόμο για το γεωτεμάχιο με στοιχεία (Α1,Α2,...,Α28,Α1) και με εμβαδόν 4973.31 τμ, ότι :

α) Είναι άρτιο κατά κανόνα . Καθίσταται οικοδομήσιμο εφόσον ο δρόμος ειναι αναγνωρισμένη οδός προ του 23 σύμφωνα με τις πολεοδομικές διατάξεις που ισχύουν σήμερα

β) βρίσκεται εκτός οικισμού στην τ.κ.ΒΑΡΝΑΚΑ της δ.ε.ΑΛΥΖΙΑΣ του Δ.ΞΗΡΟΜΕΡΟΥ της Π.Ε.ΑΙΤΩΛΟΑΚΑΡΝΑΝΙΑΣ της ΠΕΡΙΦΕΡΕΙΑΣ ΔΥΤΙΚΗΣ ΕΛΛΑΔΑΣ

γ) δεν εμπίπτει στις διατάξεις του Ν. 1337/83 που αφορούν υποχρεωτική εισφορά σε γη και χρήμα

δ) εντός της ιδιοκτησίας δεν διέρχονται σήμερα, εναέριες γραμμές μεταφοράς ρεύματος υψηλής τάσης της ΔΕΗ ή ρέμα ή αγωγός φυσικού αερίου.

ε) εντός των ομόρων γεωτεμαχίων δεν υφίστανται διατηρητέα κτίσματα

ΜΑΙΟΣ 2025
Ο ΜΗΧΑΝΙΚΟΣ

ΜΙΛΤΙΑΔΗΣ Γ. ΜΠΙΡΜΠΑΣ
ΠΤΥΧ. ΠΟΛΙΤΙΚΟΣ ΜΗΧΑΝΙΚΟΣ ΤΕ
Msc ΠΕΡΙΒΑΛΛΟΝΤΙΚΟΣ ΣΧΕΔΙΑΣΜΟΣ Ε.Α.Π.
ΜΕΛΟΣ ΕΕΤΕΜ ΑΡ. ΜΗΤΡΩΟΥ: 28053 - ΑΡΙΘΜΟΣ Τ.Ε.Ε. 78062
ΕΝΕΡΓΕΙΑΚΟΣ ΕΠΙΘΕΩΡΗΤΗΣ ΚΤΙΡΙΩΝ, Α.Μ. 11969
ΜΥΤΙΚΑΣ ΑΙΤΩΛ/ΝΙΑΣ ΤΗΛ.: 2646081344
ΑΦΜ:067843532-ΔΟΥ ΑΓΡΙΝΙΟΥ

ΘΕΟΔΩΡΟΣ ΘΕΟΧ. ΜΟΡΕΛΛΑΣ
ΔΙΠΛΩΜ. ΠΟΛΙΤΙΚΟΣ ΜΗΧΑΝΙΚΟΣ
ΠΟΛΥΤΕΧΝΕΙΟ ΠΑΤΡΩΝ
ΜΕΛΟΣ Τ.Ε.Ε - ΑΡΙΘ ΜΗΤΡ· 134010
Ι ΔΡΟΣΟΠΟΥΛΟΥ 250 - ΠΑΤΗΣΙΑ
ΑΦΜ 136002356 - Δ.Ο Υ ΓΑΛΑΤΣΙΟΥ

ΠΑΡΑΤΗΡΗΣΕΙΣ

1. Τα όρια του (Α1,Α2,...,Α28,Α1) και με εμβαδόν 4973.31 τμ και οι όμοροι του παρόντος τοπογραφικού υπεδείχθησαν υπό του ενδιαφερομενου.Τα ονόματα των φερόμενων ομόρων ιδιοκτητών & η χρονολογία δημιουργίας των ομόρων ιδιοκτησιών ελήφθησαν από τον ενδιαφερόμενο
2. Το διάγραμμα είναι ενταγμένο στο κρατικό σύστημα συντεταγμένων ΕΓΣΑ '87, συντελεστής κλίμακας: 1,000460382
3. Οι διαστάσεις και το εμβαδόν υπολογίσθηκαν αναλυτικά απο τις συντεταγμένες των κορυφών
4. Η Εξάρτηση από το Ε.Γ.Σ.Α.'87 πραγματοποιήθηκε με παρατηρήσεις που διεξήχθησαν 15/05/2025 και στο χρονικό διάστημα από 10:01π μ έως 14:10 κάνοντας χρήση του ΔΙΚΤΥΟΥ HxGN SMARTNET σε HEPOS. Η εξάρτηση έγινε με μέθοδο RTK (οριζοντιογραφία & ορθομετρικά υψόμετρα).
Για τις μετρήσεις χρησιμοποιήθηκε GNSS δέκτης XYZ X1LITE
5.Δεν έγινε έλεγχος ζώνης Γ.Γ.Υ.Π./Ορίων Natura/Απαλλοτρίωσης οδού/Άλλης Υπηρεσίας
6. ΒΡΙΣΚΕΤΑΙ ΕΚΤΟΣ ΚΗΡΥΓΜΕΝΟΥ ΑΡΧΑΙΟΛΟΓΙΚΟΥ ΧΩΡΟΥ

ΔΗΛΩΣΗ ΙΔΙΟΚΤΗΤΗ (Ν. 4030/2011)

Ο κάτωθι υπογεγραμμένος ΒΑΣΙΛΕΙΟΣ ΖΑΡΚΑΔΟΥΛΑΣ, ΓΕΩΡΓΙΟΣ ΖΑΡΚΑΔΟΥΛΑΣ & Κλήρ. ΑΝΔΡΕΑ ΖΑΡΚΑΔΟΥΛΑ δηλώνω ότι :

1. τά αρχικά και υλοποιημένα όρια του γεωτεμαχίου (Α1,Α2,...,Α28,Α1) και με εμβαδόν 4973.31 τμ, που βρίσκεται εκτός οικισμού στην τ.κ.ΒΑΡΝΑΚΑ της δ.ε.ΑΛΥΖΙΑΣ του Δ.ΞΗΡΟΜΕΡΟΥ της Π.Ε.ΑΙΤΩΛΟΑΚΑΡΝΑΝΙΑΣ της ΠΕΡΙΦΕΡΕΙΑΣ ΔΥΤΙΚΗΣ ΕΛΛΑΔΑΣ , υπεδείχθησαν από εμάς από τον ΒΑΣΙΛΕΙΟ ΖΑΡΚΑΔΟΥΛΑ και
2. ευθύνομαστε για την ακρίβεια των δηλουμένων ορίων του γεωτεμαχίου και για την ύπαρξη και την αιτία του δικαιώματός μας να ζητήσουμε την έκδοση τοπογραφικού διαγ/τος.

ΜΑΡΤΙΟΣ 2025
Ο ΔΗΛΩΝ

BIRBAS
MILTOS
CONSTRUCTION & DEVELOPMENT

ΤΕΧΝΙΚΟ ΓΡΑΦΕΙΟ
ΜΙΛΤΙΑΔΗΣ ΜΠΙΡΜΠΑΣ & ΣΥΝΕΡΓΑΤΕΣ ΜΗΧΑΝΙΚΟΙ

μελέτες - επίβλεψη - κατασκευή - ενεργειακή επιθεώρηση
αποτυπώσεις - χαράξεις τεχνικών έργων

www.birbas.gr

Εργοδότης
ΖΑΡΚΑΔΟΥΛΑΣ ΒΑΣΙΛΕΙΟΣ
ΖΑΡΚΑΔΟΥΛΑΣ ΓΕΩΡΓΙΟΣ
κληρ. ΖΑΡΚΑΔΟΥΛΑ ΑΝΔΡΕΑ

Έργο
ΑΠΟΤΥΠΩΣΗ ΓΗΠΕΔΟΥ ΕΚΤΟΣ ΟΡΙΩΝ ΟΙΚΙΣΜΟΥ
ΚΑΕΚ 010450301067

Θέση
ΘΕΣΗ "ΛΥΓΙΕΣ" ΕΚΤΟΣ ΟΙΚΙΣΜΟΥ
Τ.Κ. ΒΑΡΝΑΚΑ - Δ.Ε. ΑΛΥΖΙΑΣ ΔΗΜΟΣ ΞΗΡΟΜΕΡΟΥ
Π.Ε. ΑΙΤΩΛΟΑΚΑΡΝΑΝΙΑΣ - ΠΕΡΙΦΕΡΕΙΑ ΔΥΤΙΚΗΣ ΕΛΛΑΔΑΣ

Θέμα Σχεδίου
ΤΟΠΟΓΡΑΦΙΚΟ ΔΙΑΓΡΑΜΜΑ

Ημερομηνία
ΜΑΙΟΣ 2025

Κλίμακα Σχεδίασης
1:500

Αριθμός Σχεδίου
A_1

Ομάδα Μελέτης :
ΜΠΙΡΜΠΑΣ ΜΙΛΤΙΑΔΗΣ ΠΤΥΧ. ΠΟΛΙΤΙΚΟΣ ΜΗΧΑΝΙΚΟΣ ΤΕ MSc

Σφραγίδα Μελετητή

ΜΙΛΤΙΑΔΗΣ Γ. ΜΠΙΡΜΠΑΣ
ΠΤΥΧ. ΠΟΛΙΤΙΚΟΣ ΜΗΧΑΝΙΚΟΣ ΤΕ
Msc ΠΕΡΙΒΑΛΛΟΝΤΙΚΟΣ ΣΧΕΔΙΑΣΜΟΣ Ε.Α.Π.
ΜΕΛΟΣ ΕΕΤΕΜ ΑΡ. ΜΗΤΡΩΟΥ: 28053 - ΑΡΙΘΜΟΣ Τ.Ε.Ε. 78062
ΕΝΕΡΓΕΙΑΚΟΣ ΕΠΙΘΕΩΡΗΤΗΣ ΚΤΙΡΙΩΝ, Α.Μ. 11969
ΜΥΤΙΚΑΣ ΑΙΤΩΛ/ΝΙΑΣ ΤΗΛ.: 2646081344
ΑΦΜ:067843532-ΔΟΥ ΑΓΡΙΝΙΟΥ